
总平面 / 两次到达的空间差异

1:200 / 5 m 网格 / 南低北高 / 两个入口互不直视

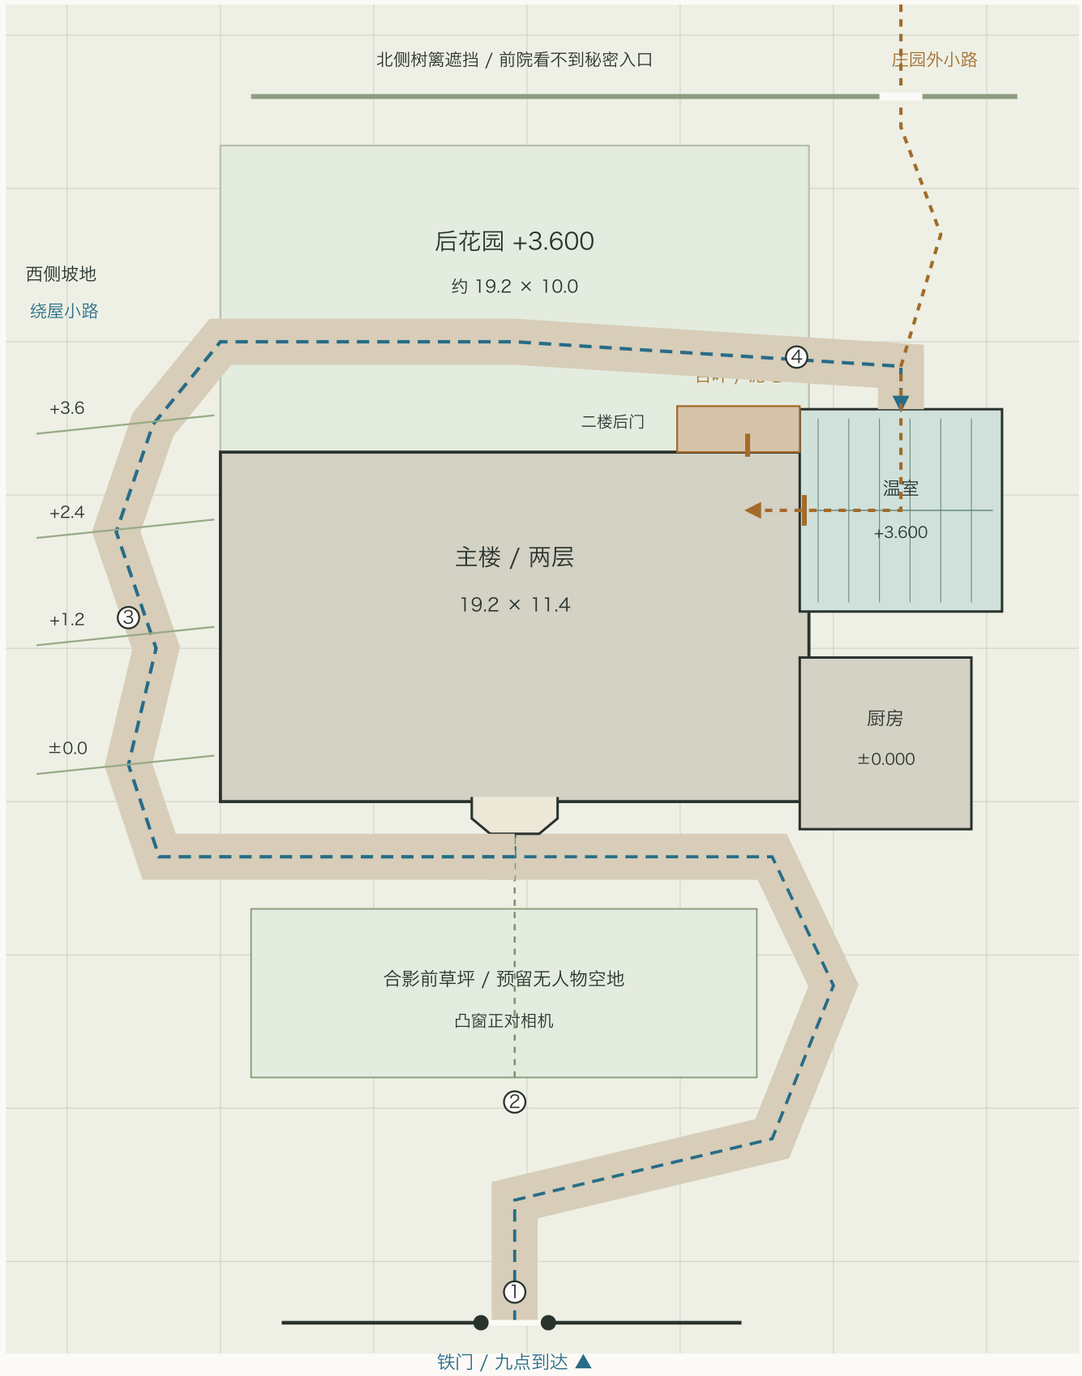

铁门 / 九点到达 ▲

N

01 房子是案件的一部分

前院 ±0.000 → 正门。
后园 +3.600 → 温室。
两次到达由地形区分。

02 玩家日常环线

门厅 → 楼梯 → 后门，
花园 → 温室 → 西侧小路，
回到前院与门厅。

03 秘密路线

北侧外部小路直接入温室。
经过内闩侧门到暗房。
全程不经过主屋公共区。

04 透视机位编号


① 铁门外 / 雨夜
② 前草坪 / 秋日下午
③ 西侧坡路 / 雨夜
④ 后花园物证 / 雨夜

1:200 / 每格 5 m

0 1 5 m

一楼 / 公共空间与声音线索

前院 ±0.000 / 餐厅向后延伸至暗房下方

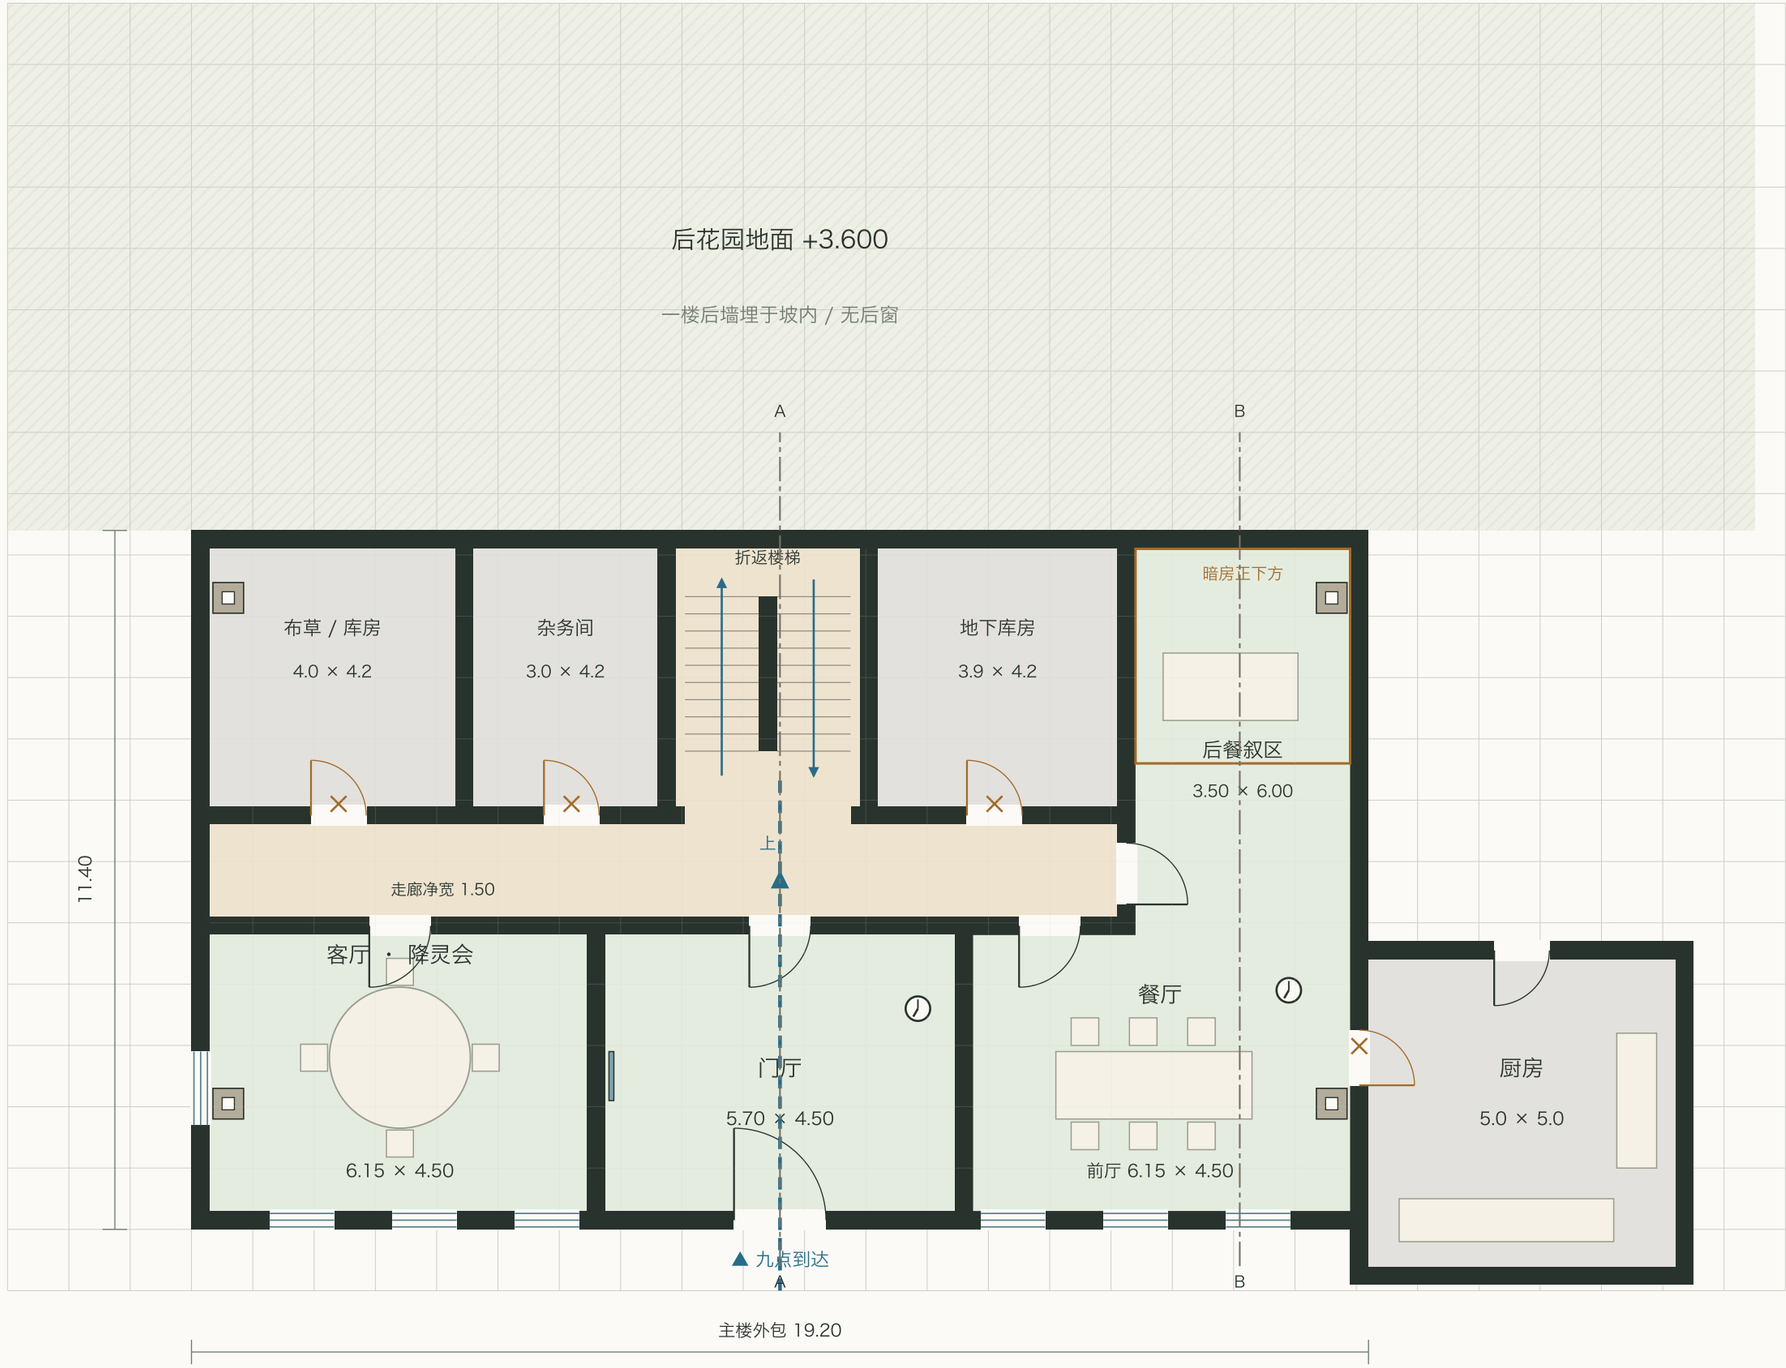

N

01 餐厅扩展

前厅保留朝南采光。
沿东侧向后延伸，
餐叙区在暗房正下方。

02 日常与案件重叠

康斯坦斯仍在餐厅。
楼上的碎响 / 铃声，
沿楼板与东侧空间传来。

03 关卡开放

0B：一楼与花园。
0C 后：楼梯与二楼开放。
锁门房间保留宅邸可信感。

04 楼梯尺寸

占地 3.00 × 4.20。
20 级 × 0.18 = 3.60。
两跑，踏步 0.28。
每跑净宽 1.20。

探索权限 / 门的状态

- 可进入探索
- 只能走过
- 不能进入

× 锁门 ┃ 暗房一侧门闩


圆形指针：钟 / 蓝短线：镜子

1:100 / 每格 1 m

0 1 5 m

二楼 / 调查环线与秘密入口

楼面 +3.600 / 与后花园同高 / 正立面朝南

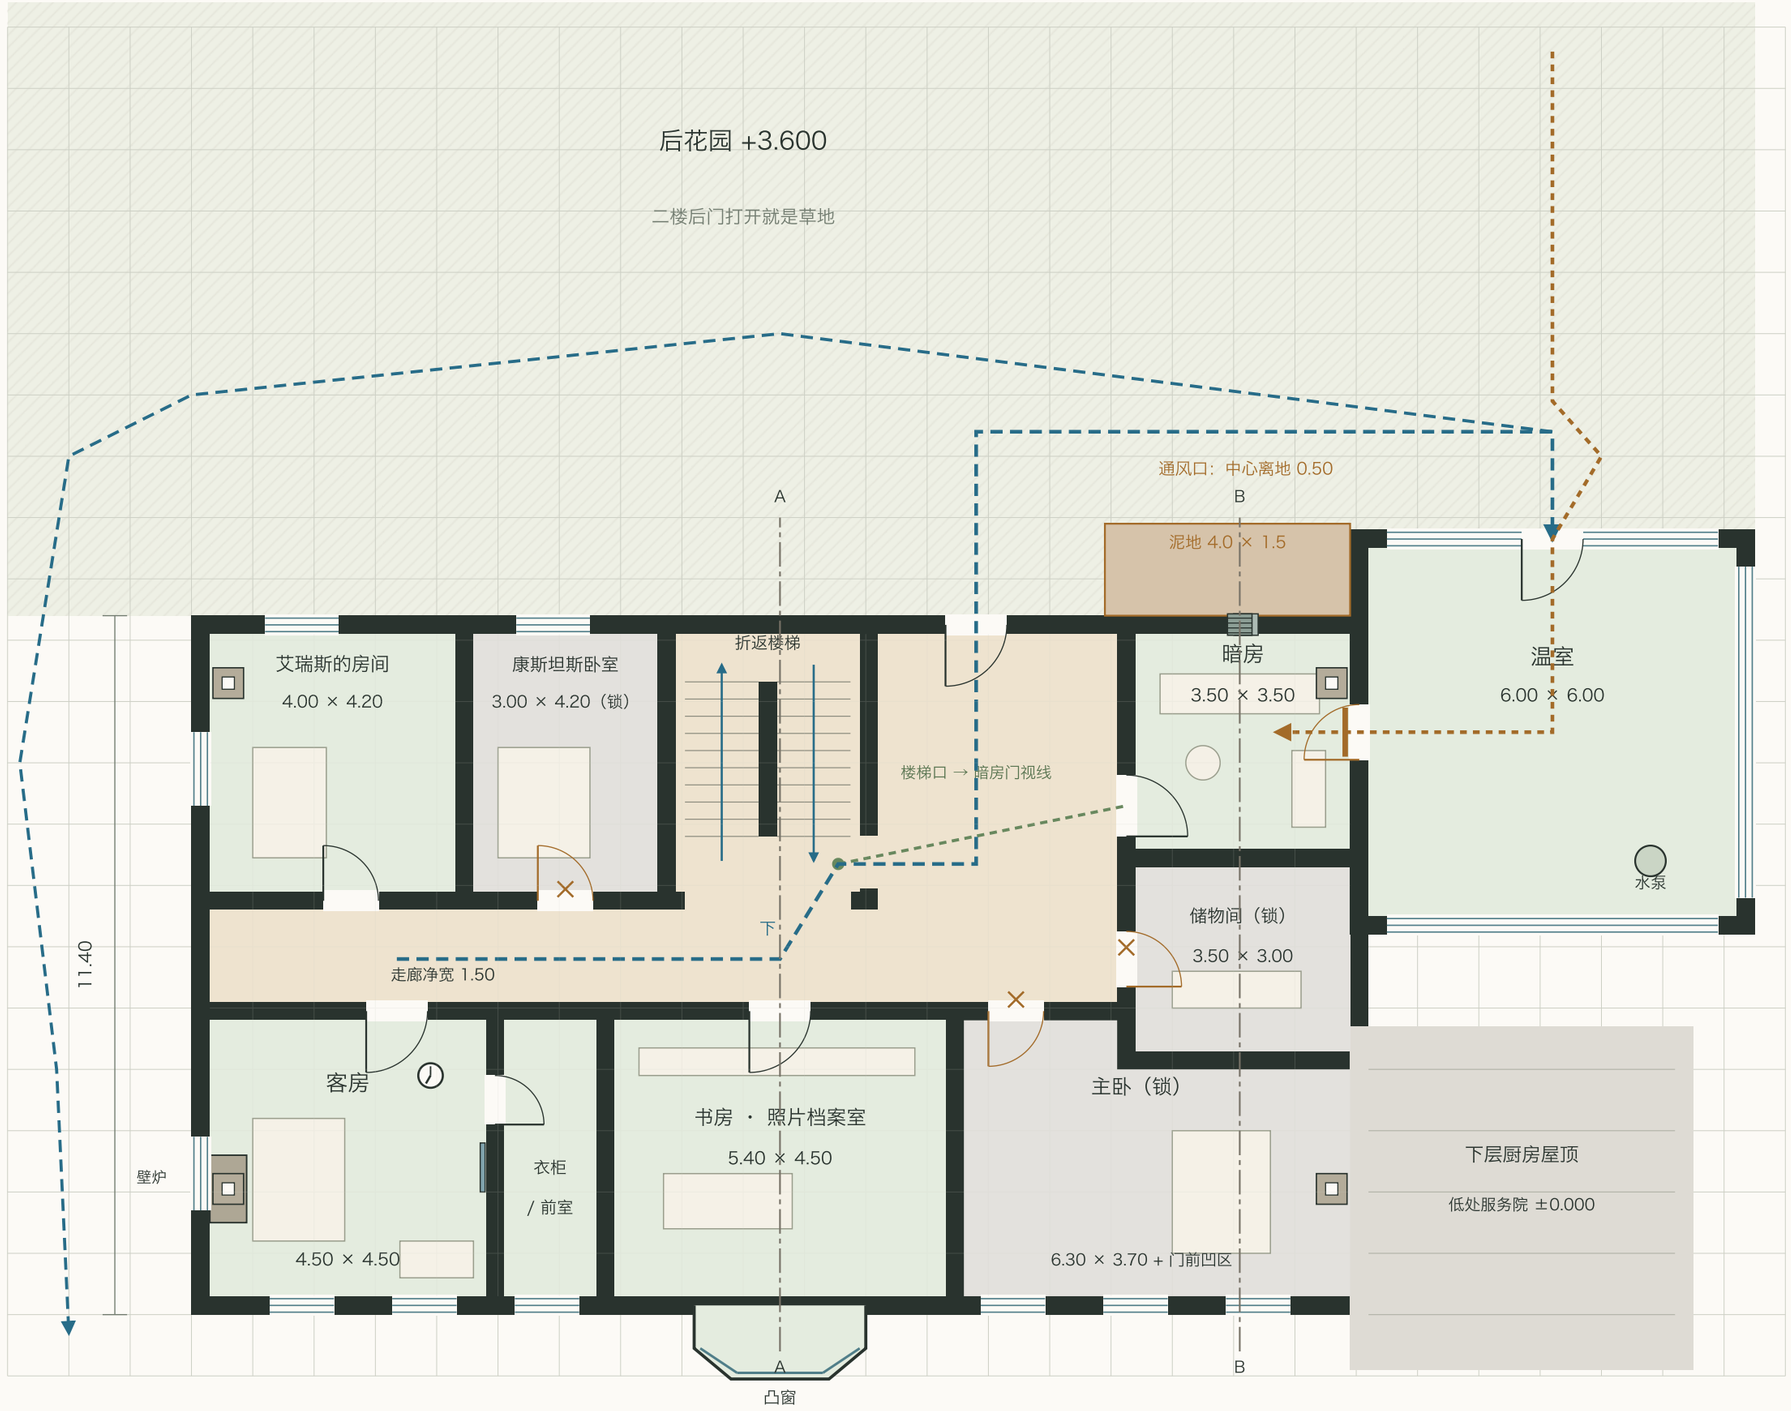

01 两个地面

正门在低处 ±0.000。
后园在高处 +3.600。
后花园就是二楼室外。

02 密室的三个接口

走廊门：正常可达。
温室侧门：暗房内侧闩。
后墙百叶：0.40 × 0.40。

03 视线公平性

从客房出门必经公共区。
楼梯口到暗房门无阻挡。
门缝红光可以被看见。

04 两条路线

蓝虚线：玩家日常环线。
赭虚线：秘密进入路径。
外侧小路与前院不相交。

探索权限 / 门的状态

可进入探索
只能走过
不能进入

× 锁门 | 暗房一侧门闩

圆形指针：钟 / 蓝短线：镜子


1:100 / 每格 1 m

0 1 5 m


剖面 / 两个地面与楼上楼下

1:100 / A-A 中轴：正门、门厅与楼梯 / B-B 东侧：餐厅、暗房与百叶

A-A

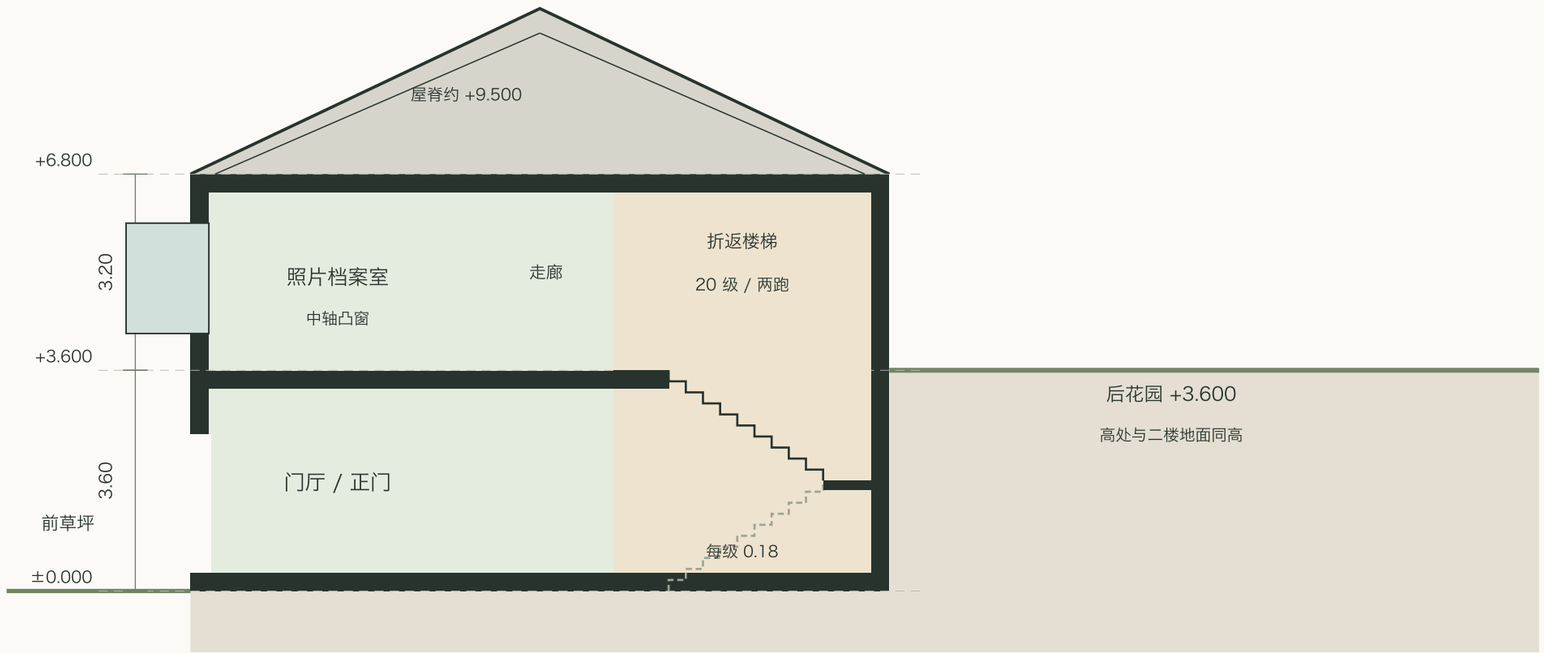

B-B

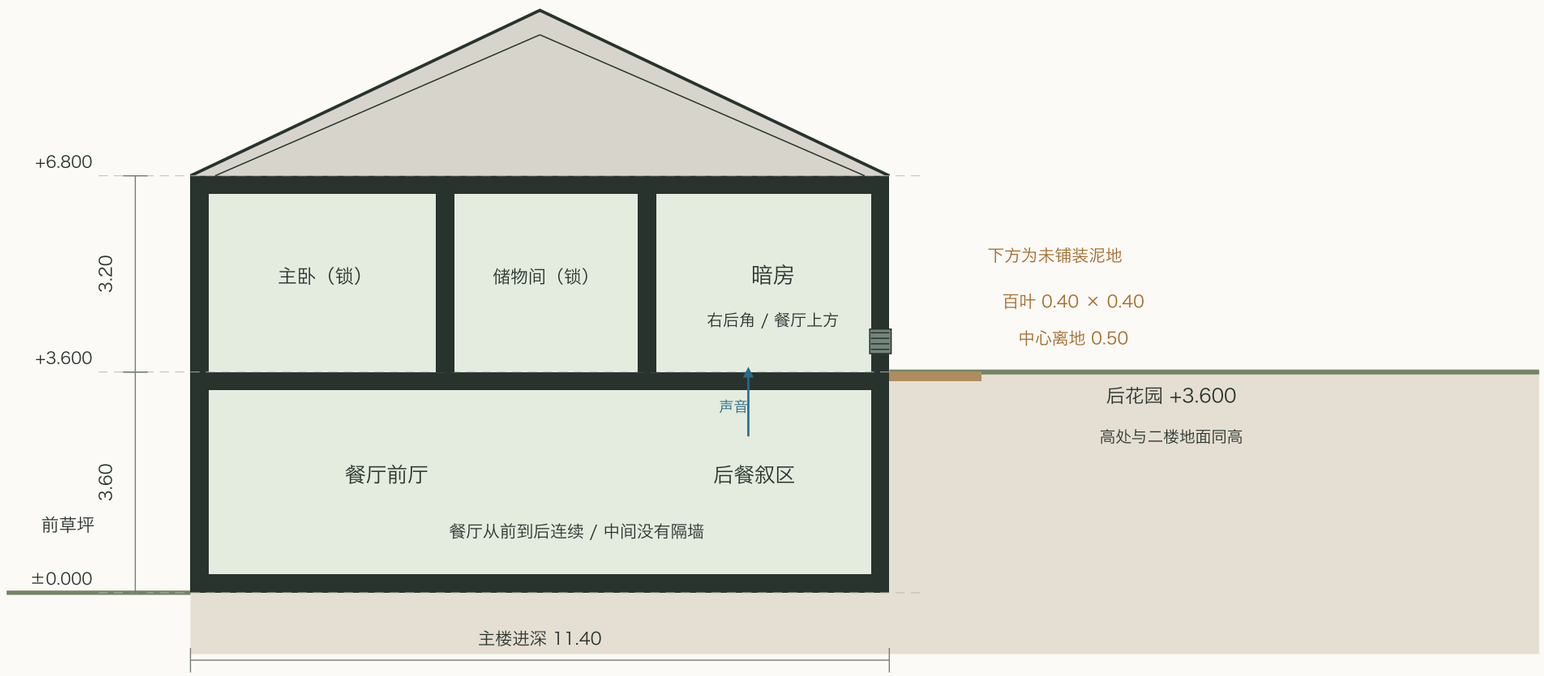

01 两条真实剖切线

两条剖线均在平面标出。
中轴与暗房不在同一直线上。
因此在同张图分别剖开。

02 高度基准

低处前院 ±0.000。
二楼、后园、温室 +3.600。
主楼前两层 / 后只露上层。

03 空间让证词成立

餐叙区与暗房上下相叠。
窗台、百叶、泥地在同侧。
温室共墙侧门见二楼平面。

04 设计图的边界

层高为楼面到楼面。
楼板示意厚 0.30。
不包含结构、排水施工。

1:100 / 每格 1 m

0 1 5 m